

PORTAFOLIO



Sobre mi.

Hola, mi nombre es Giovanni Luna García. Soy arquitecto recién egresado de la Universidad Autónoma de Ciudad Juárez (UACJ) y me encuentro radicado en Ciudad Juárez, Chihuahua.

Mi flujo de trabajo se apoya en plataformas BIM y CAD como Revit, AutoCAD y SketchUp, complementado con herramientas de representación gráfica y renderizado de alta calidad como InDesign, Photoshop, Lumion, V-Ray, D5 Render y Enscape.

Además de mi formación arquitectónica, cuento con experiencia práctica en la parte operativa y administrativa, manejando logística de inventarios, gestión de compras y apoyo en instalaciones.

En cuanto a mis intereses de diseño, me identifico profundamente con la arquitectura Mid-Century Modern, el diseño urbano, el interiorismo y la integración del paisajismo en entornos áridos. A nivel personal, me considero una persona metódica y disciplinada, impulsada por mi gusto por el aprendizaje continuo, la investigación histórica, la geopolítica y el entrenamiento físico.



Experiencia

CVending S.A. de C.V .

Asistente de Operaciones y Logística.

- Gestión y adquisición de insumos para la operación continua, coordinando pedidos semanales y manteniendo un margen de error mínimo en el inventario.
- Elaboración de control de stock para diversas categorías de productos, previniendo desabastos en periodos de alta demanda.
- Supervisión del registro de compraventa y flujo de mercancía, optimizando el tiempo de conciliación de entradas y salidas.

Proyectista Independiente.

Diseñador Arquitectónico.

- Desarrollo integral de proyectos arquitectónicos y ejecutivos de pequeña escala, coordinando desde la concepción espacial hasta los detalles constructivos.
- Ejecución de levantamientos en sitio y digitalización técnica, garantizando levantamientos con un alto nivel de precisión dimensional para la elaboración de planos base.
- Producción de visualizaciones 3D y renders de alta fidelidad, elaborando material gráfico representativo para la validación de diseño e integración en entregas formales.

Imagen Diagnóstica.

Asistente Administrativo y de Atención.

- Control de inventarios de insumos, realizando verificaciones periódicas para mantener el stock alineado con la demanda diaria.
- Organización y archivo de expedientes bajo normatividad institucional, reduciendo tiempos de búsqueda y mejorando el flujo de información interna.
- Gestión de la atención al público, recibiendo y orientando a los usuarios con un enfoque de calidad en el servicio.

MC Estudios y Proyectos.

Dibujante Técnico y Modelador de Instalaciones

- Desarrollo y digitalización de planos constructivos, incluyendo criterios estructurales y planos arquitectónicos detallados para proyectos de la firma.
- Modelado y representación tridimensional de isométricos, especializándome en la integración visual de instalaciones hidráulicas, sanitarias y de gas.
- Elaboración de planos ejecutivos de instalaciones (MEP) y eléctricas, garantizando la correcta lectura técnica, simbología y representación gráfica para procesos de ejecución en obra



Contactos



+52 6562567073



<https://www.linkedin.com/in/arq-giovanny-luna>



gio-luna-garcia@hotmail.com



Ciudad Juárez, Chihuahua, México

Trabajos

01.

Proyecto en Revit.

Centro de Convenciones del Desierto.
02.

Reactivación Urbano-Espacial.


Pabellón de Arquitectura.
03.

Proyecto de Renderizado.

Proyecto Casa Alas y Raíces - Estudio de Música.
04.

Departamentos.

Tipologías de Departamentos.

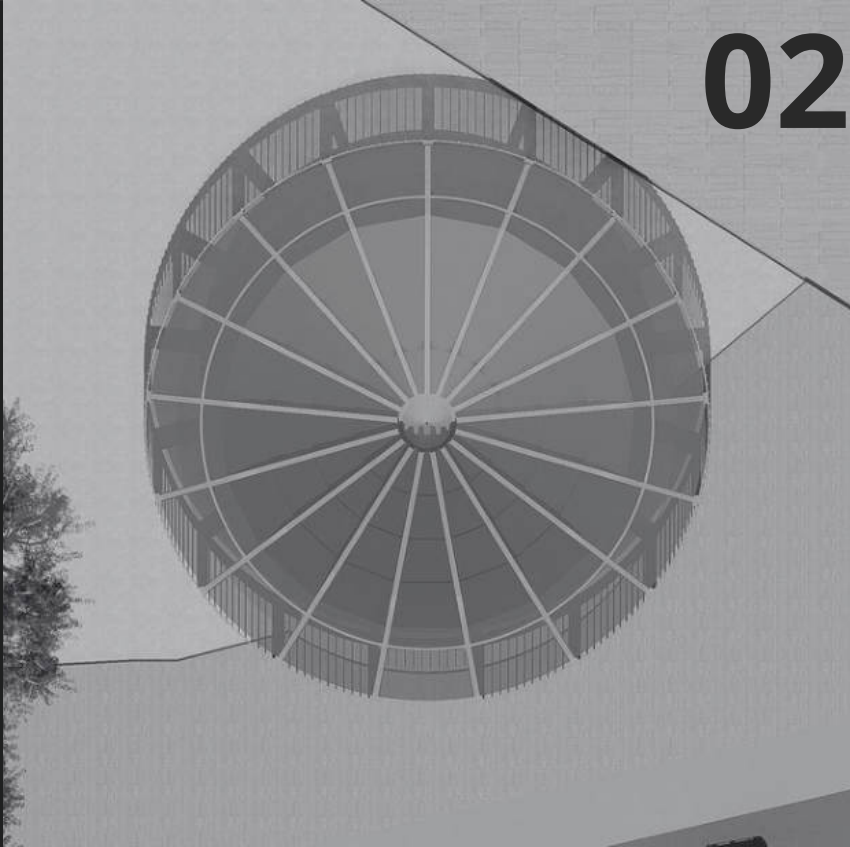


Centro de Convenciones del Desierto.

El Centro de Convenciones del Desierto, nace para responder a la falta de infraestructura especializada en eventos internacionales, científicos e industriales en la ciudad, impulsando el desarrollo económico, social y la innovación binacional. Ubicado estratégicamente en el centro-sur urbano, el proyecto busca ser un catalizador cultural y un símbolo de identidad fronteriza con criterios de sostenibilidad. Arquitectónicamente, se concibe como una extensión del paisaje árido, inspirándose en la formación mineral de la rosa del desierto para definir su materialidad y conjunto. Su idea rectora parte de una retícula ortogonal y el concepto de la línea como principio ordenador, creando un tejido flexible que combina ritmos de luz, sombra y serenidad con variaciones volumétricas que rompen la monotonía sin perder la coherencia geométrica.



Planta de Conjunto.

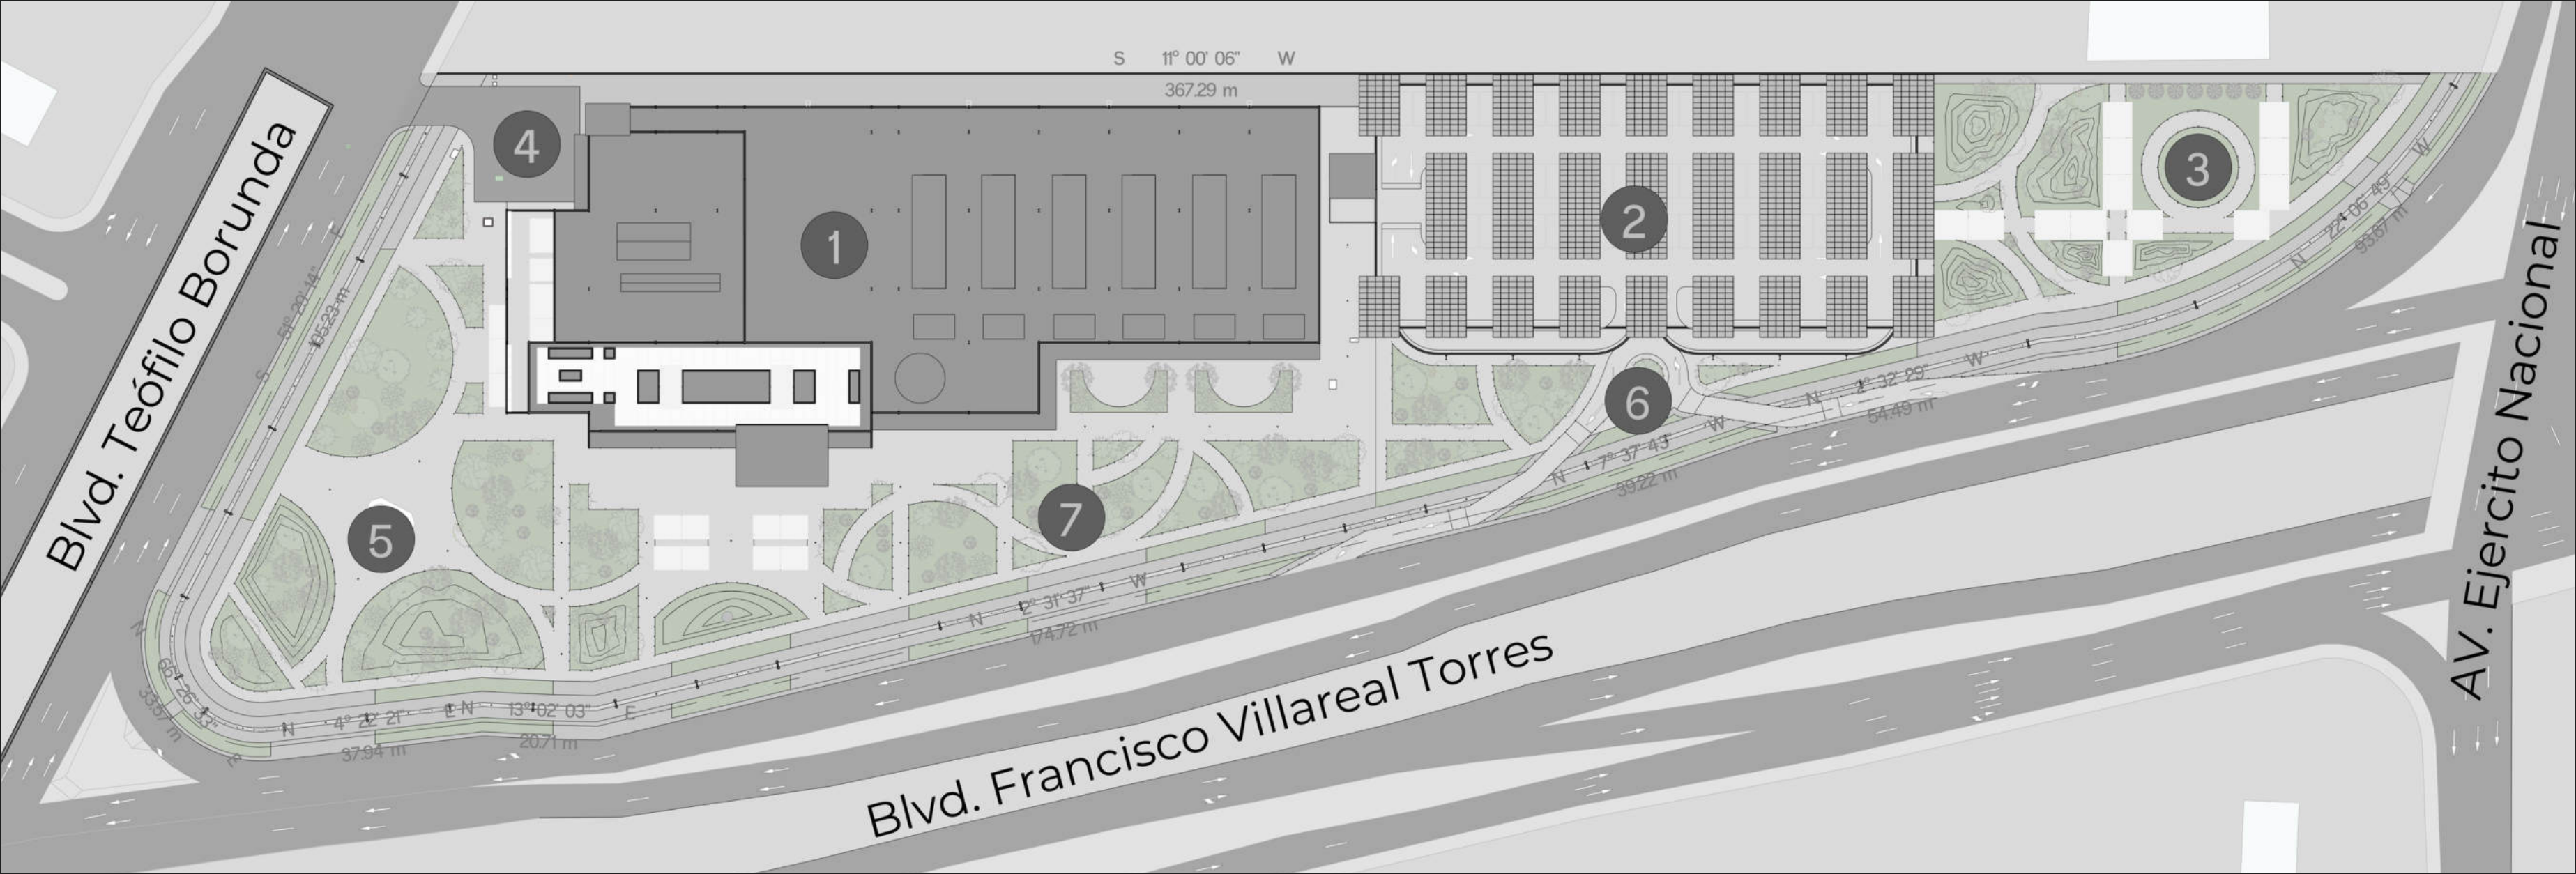

Simbología.

- 1

Edificio principal
- 2

Edificio de Estacionamiento.
- 3

Área de jardín Norte.
- 4

Área de carga y descarga.

5

Área de jardín Sur.

6

Acceso a Estacionamiento.


7

Área de jardín Este.


Fachadas.




Fachada Este Vista 1.

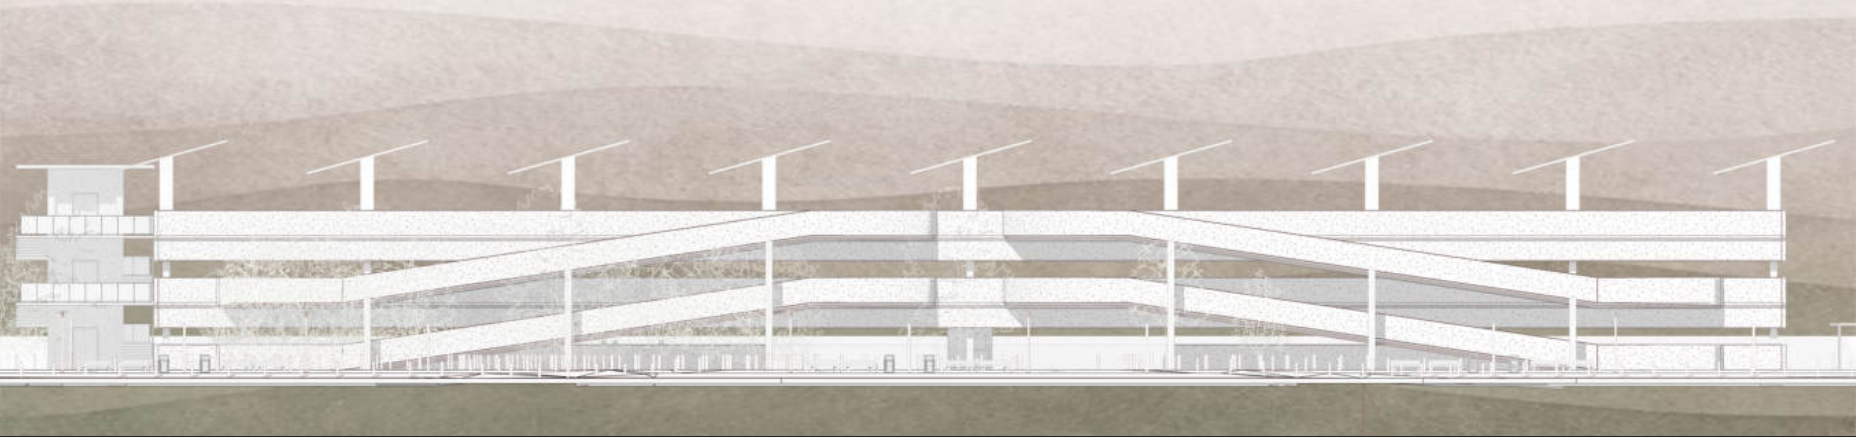

Fachada Este Vista 2.

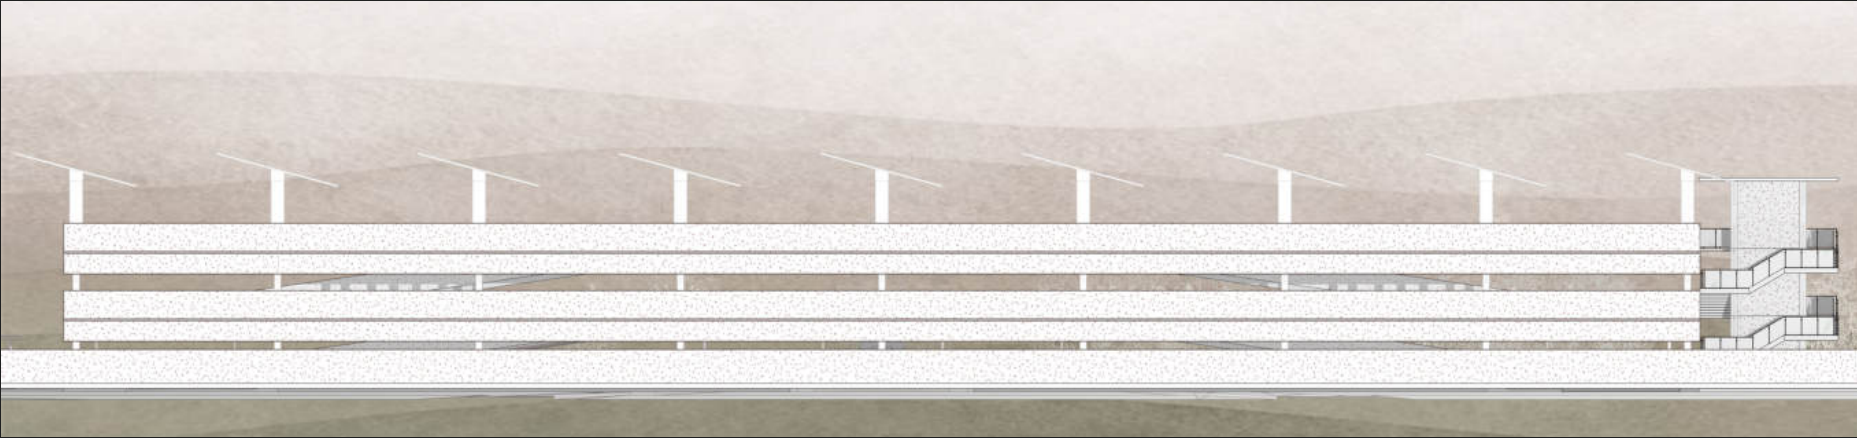

Fachada Oeste Vista 1.

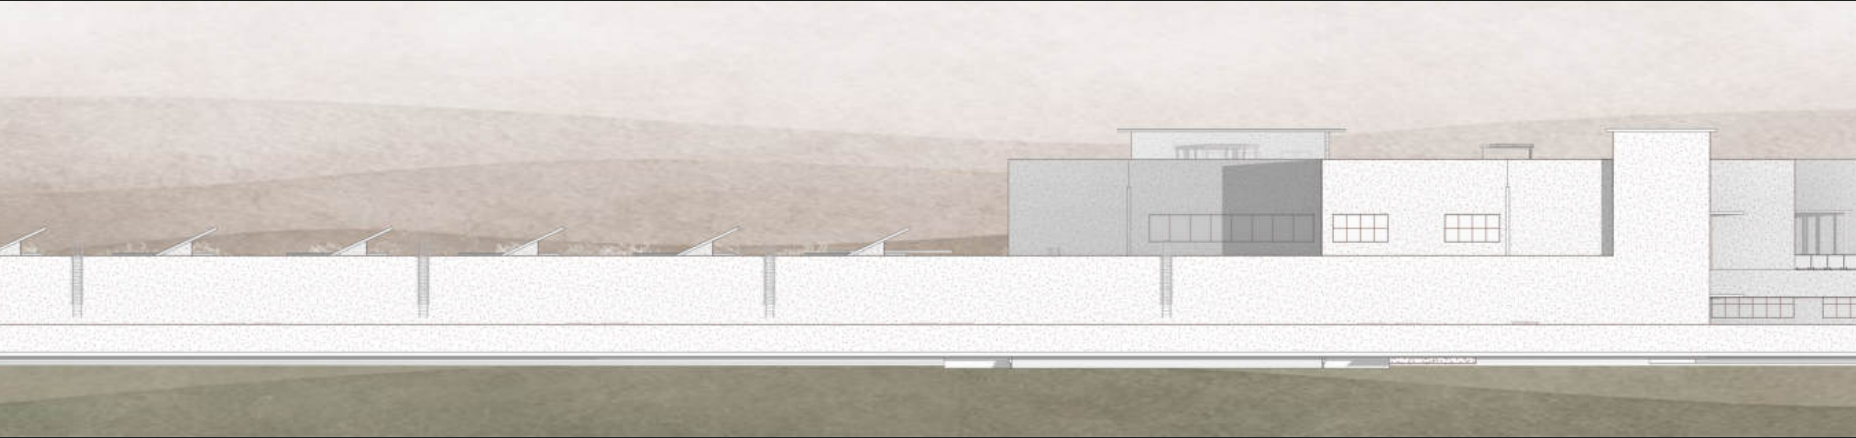

Fachada Oeste Vista 2.



Fachada Norte.




Fachada Sur..

Fachadas.



Vista Exterior.

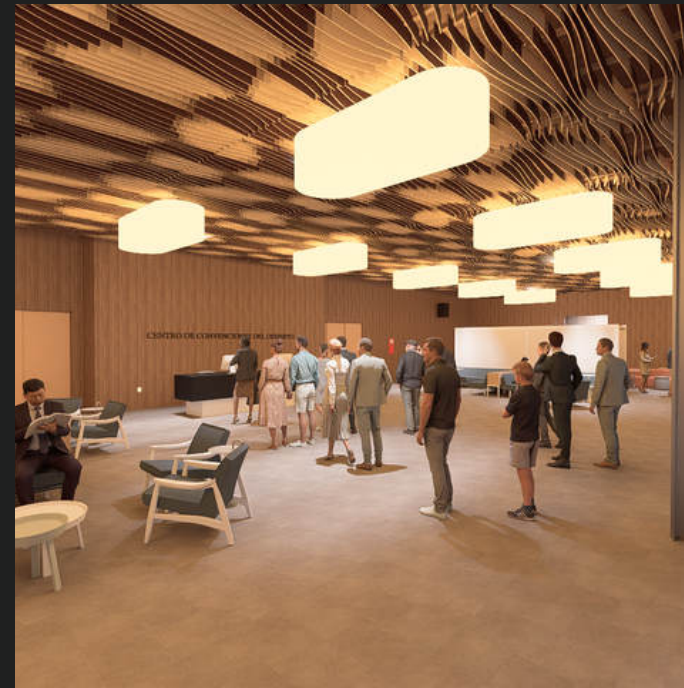

Vista Área de Recepción P.B.



Vista Sala 1.



Vista Sala 2.




Vista Sala 3.



Vista Pasillo Central.




Vista P.A. Área de Espera

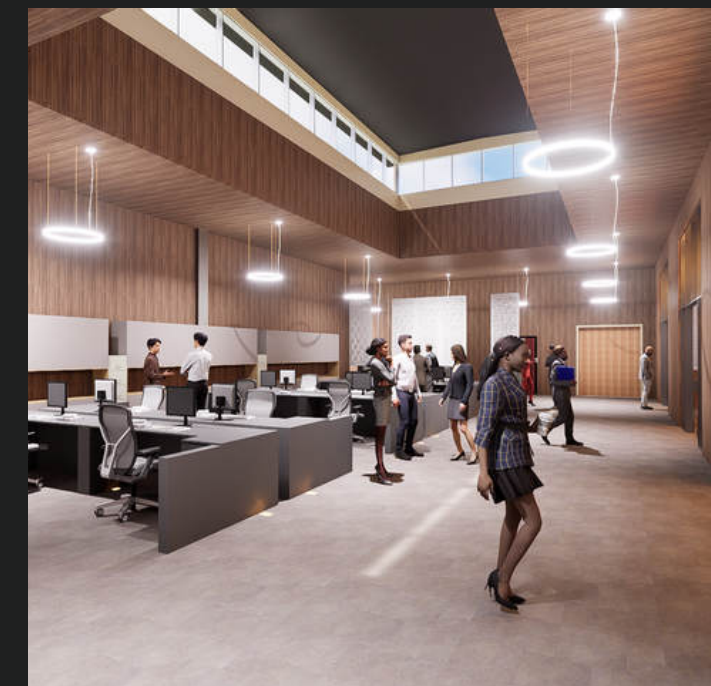


Vista Área Administrativa

Pabellón de Arquitectura.

El proyecto busca rehabilitar el anfiteatro de un museo histórico en Ciudad Juárez, transformándolo en un espacio funcional y accesible durante todo el año, sin importar las inclemencias del clima como el intenso calor o el frío. Se propone el diseño de un pabellón circular que se integra de manera sensible en el entorno existente, dialogando con la geometría y la forma curva del museo, promoviendo la apropiación del espacio por parte de la ciudadanía para diversas actividades culturales.

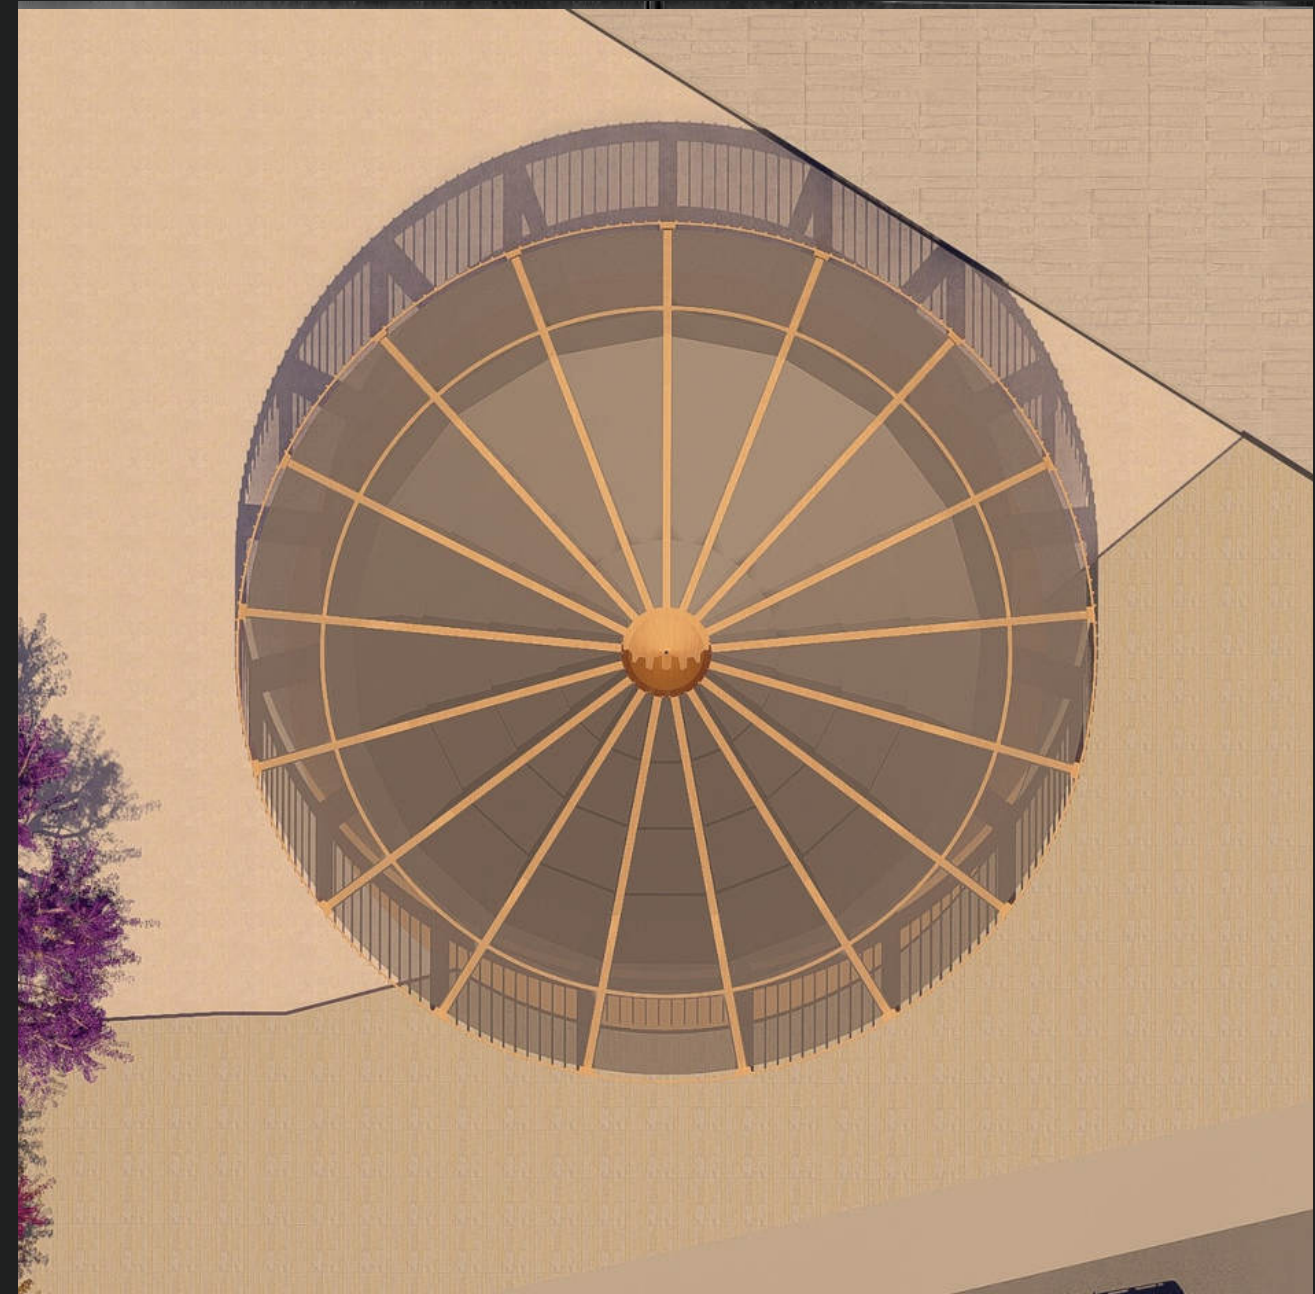


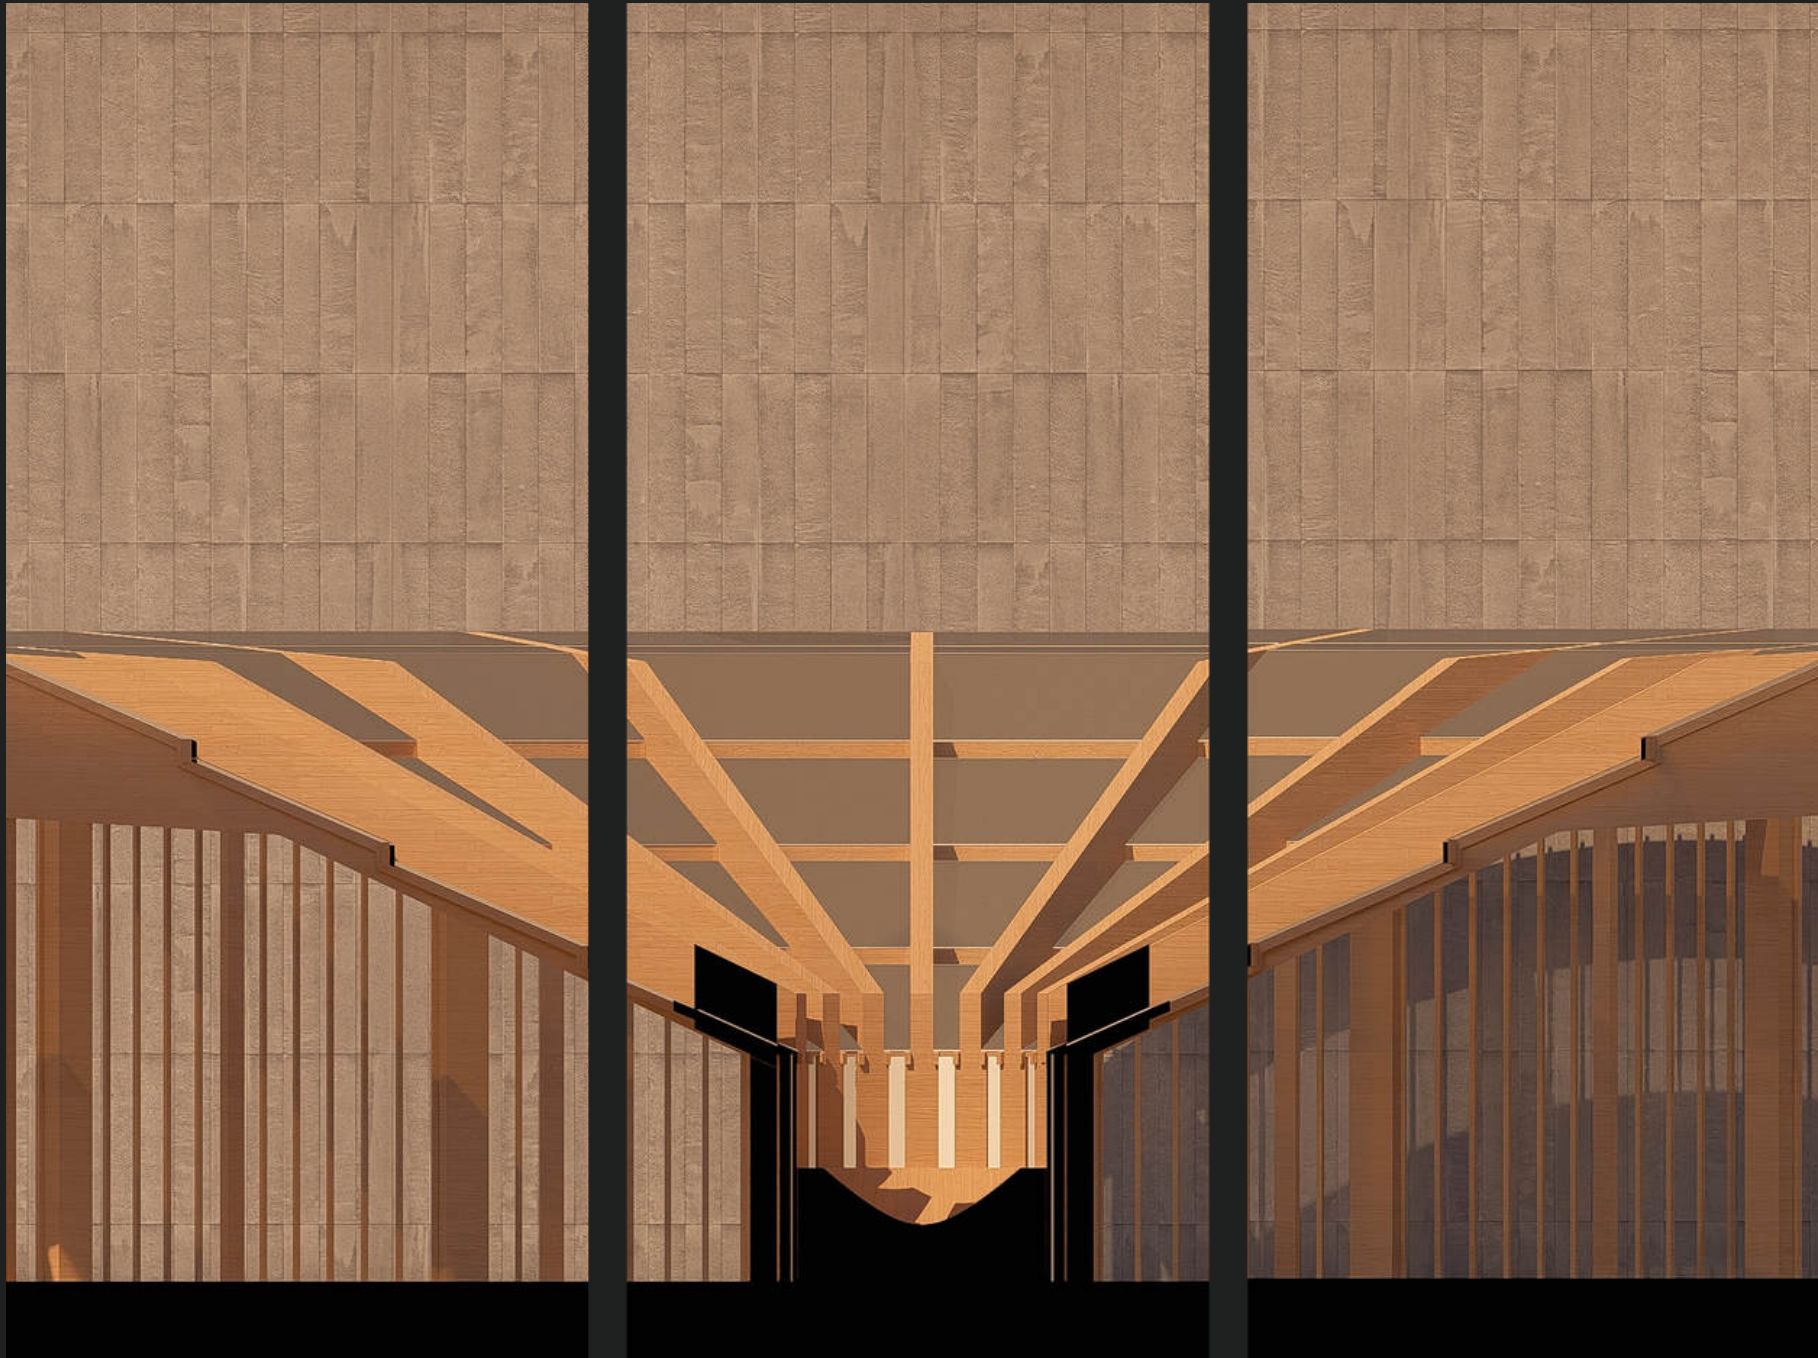

Cubierta.

La cubierta, esta es circular, rodea todo el pabellón y se va estrechando hacia el centro, permitiendo canalizar el agua de lluvia para su captación y posterior aprovechamiento en el riego de plantas.

Fachadas.

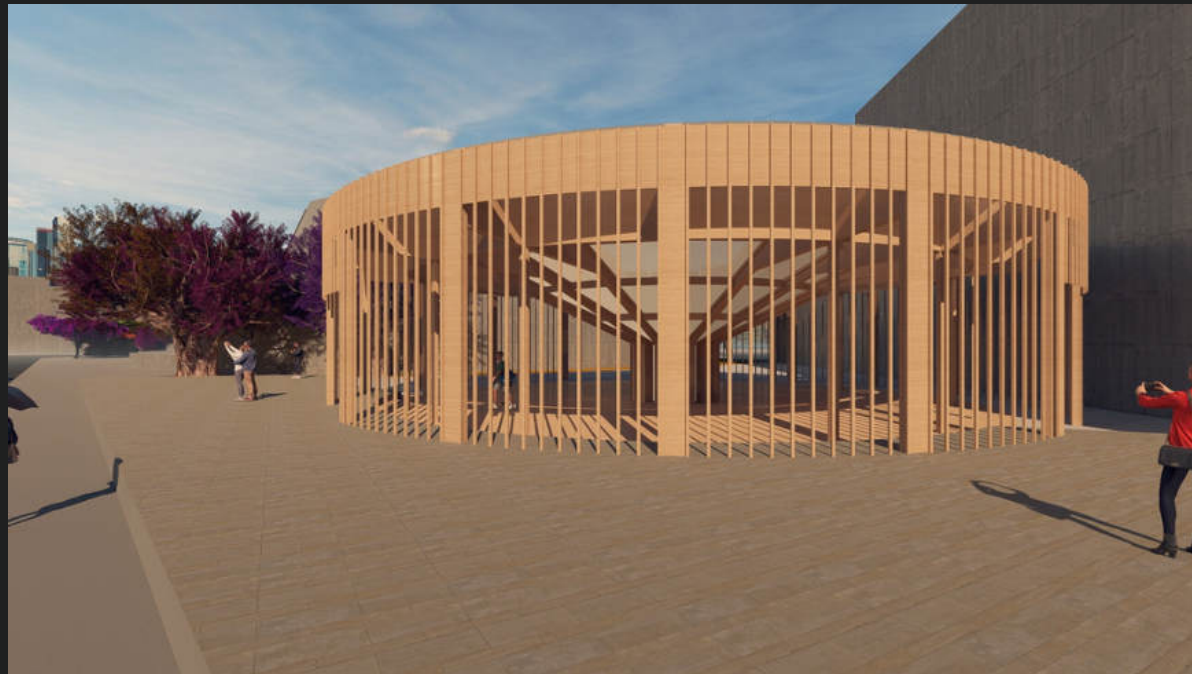

Vista Exterior 1.



Vista Exterior 2.




Vista Exterior 3.



Vista Posterior.



Vista Interior 1.

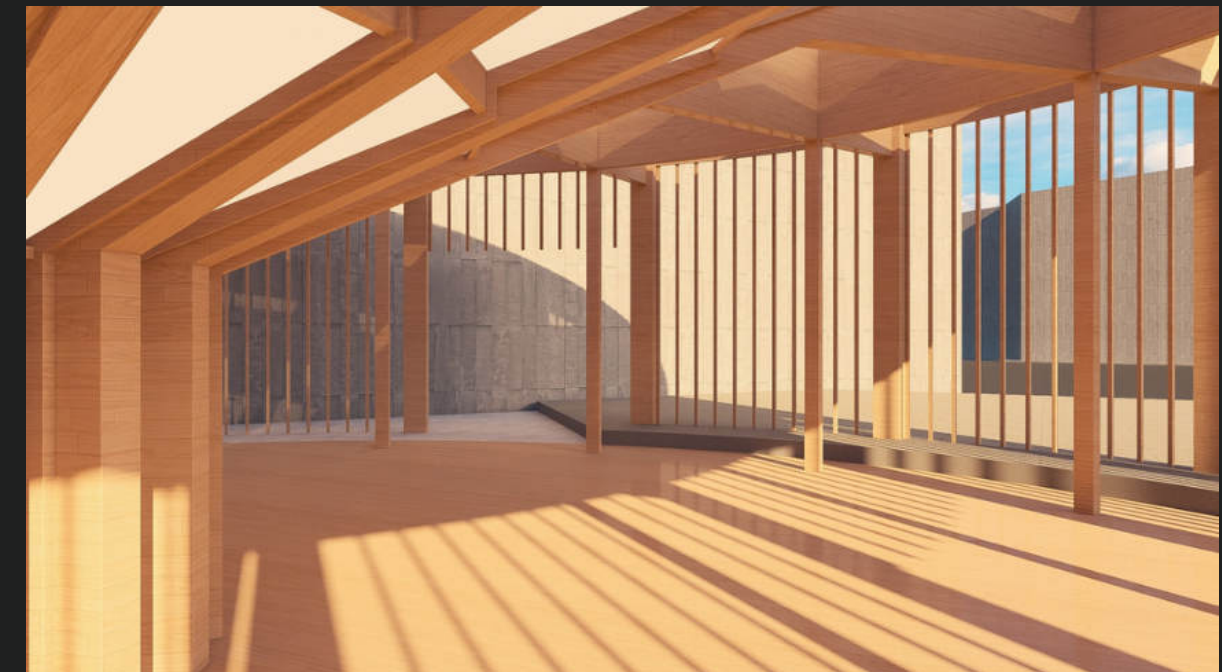

Vista Interior 2.

Casa Alas y Raíces - Estudio de Música.

Este proyecto es un ejercicio de cirugía interiorista y optimización ambiental. En lugar de alterar drásticamente la planta arquitectónica, la propuesta se enfoca en potenciar la riqueza volumétrica de la vivienda, refinando los detalles materiales y la calidad del espacio. Por su parte, el estudio de música se concibe como un santuario acústico y estético donde la luz es la protagonista. La intervención combina el diseño de iluminación interior y exterior con la máxima precisión técnica, logrando ambientes envolventes que elevan la experiencia de habitar.



Vistas del Proyecto.



Vista Exterior Día Casa Alas y Raíces.



Vista Patio Noche Casa Alas y Raíces.



Vista Exterior Noche Casa Alas y Raíces.




Vista Cocina Día Casa Alas y Raíces.

Vistas del Proyecto.



Vista Interior Noche Estudio de Música.

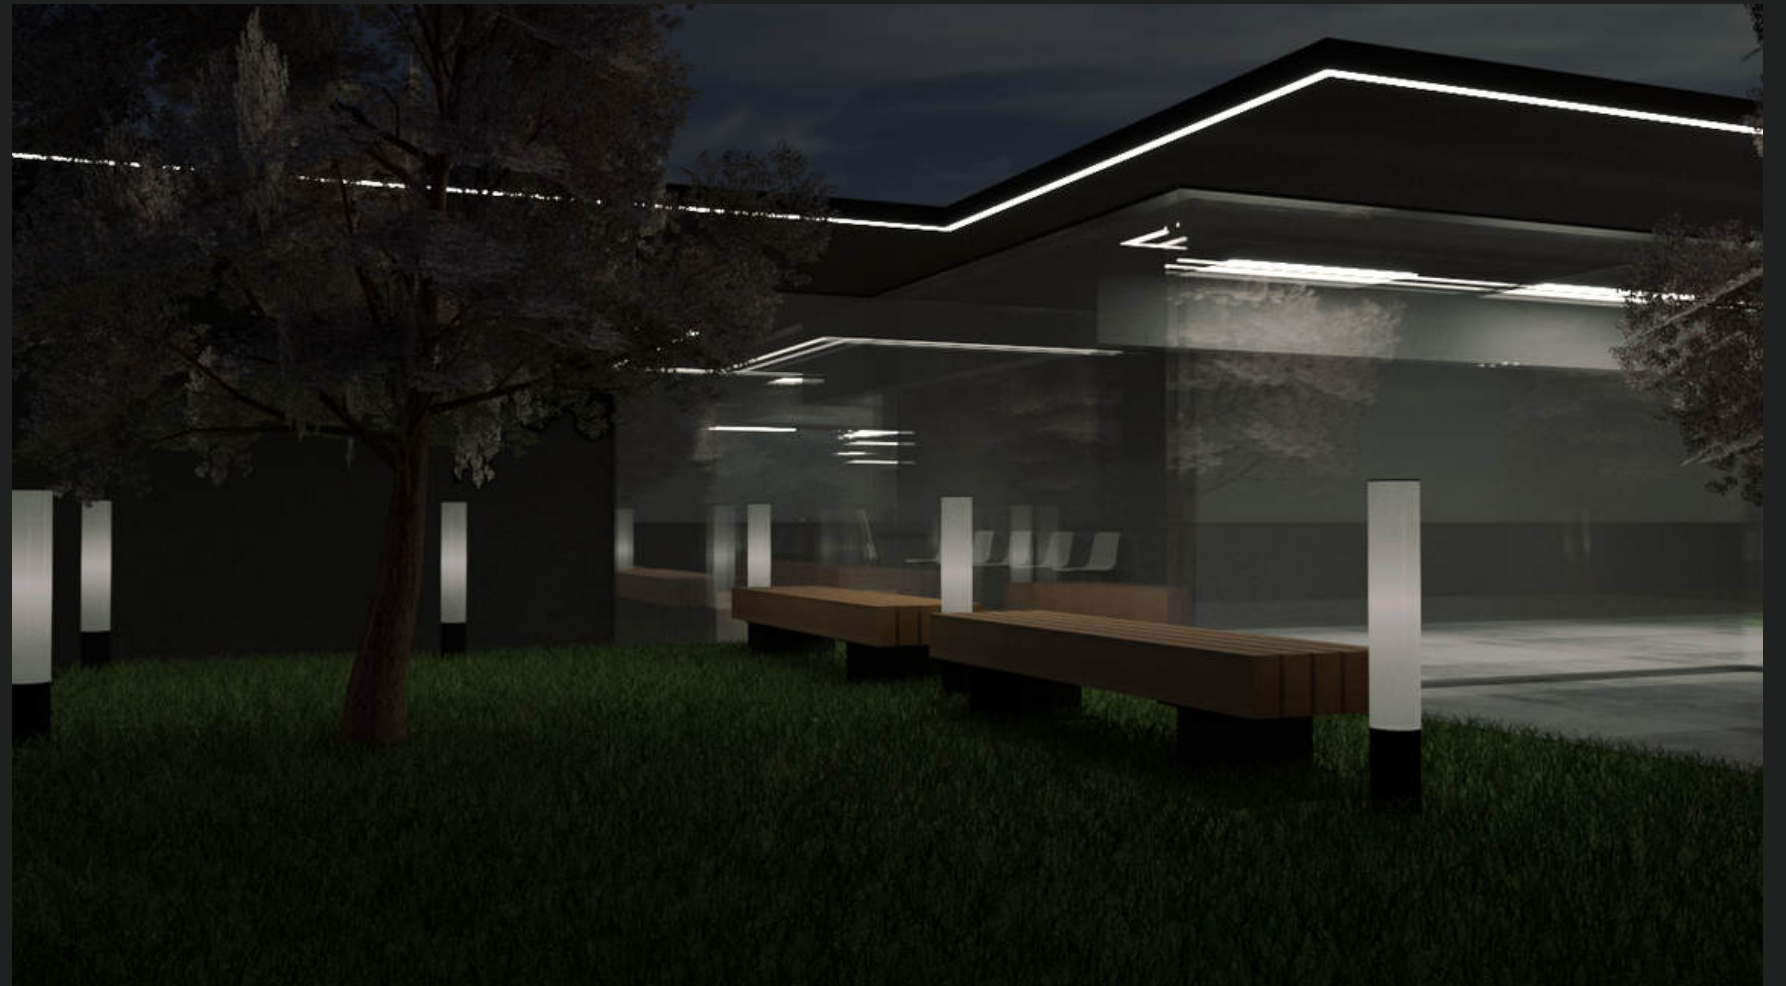

Vista Exterior Noche Estudio de Musica.

Tipologías de Departamentos.

El Centro de Convenciones del Desierto, nace para responder a la falta de infraestructura especializada en eventos internacionales, científicos e industriales en la ciudad, impulsando el desarrollo económico, social y la innovación binacional. Ubicado estratégicamente en el centro-sur urbano, el proyecto busca ser un catalizador cultural y un símbolo de identidad fronteriza con criterios de sostenibilidad. Arquitectónicamente, se concibe como una extensión del paisaje árido, inspirándose en la formación mineral de la rosa del desierto para definir su materialidad y conjunto. Su idea rectora parte de una retícula ortogonal y el concepto de la línea como principio ordenador, creando un tejido flexible que combina ritmos de luz, sombra y serenidad con variaciones volumétricas que rompen la monotonía sin perder la coherencia geométrica.



Tipologías.




Nivel 1

Tipo 1: 60 m²




1/2 Nivel

Tipologías.

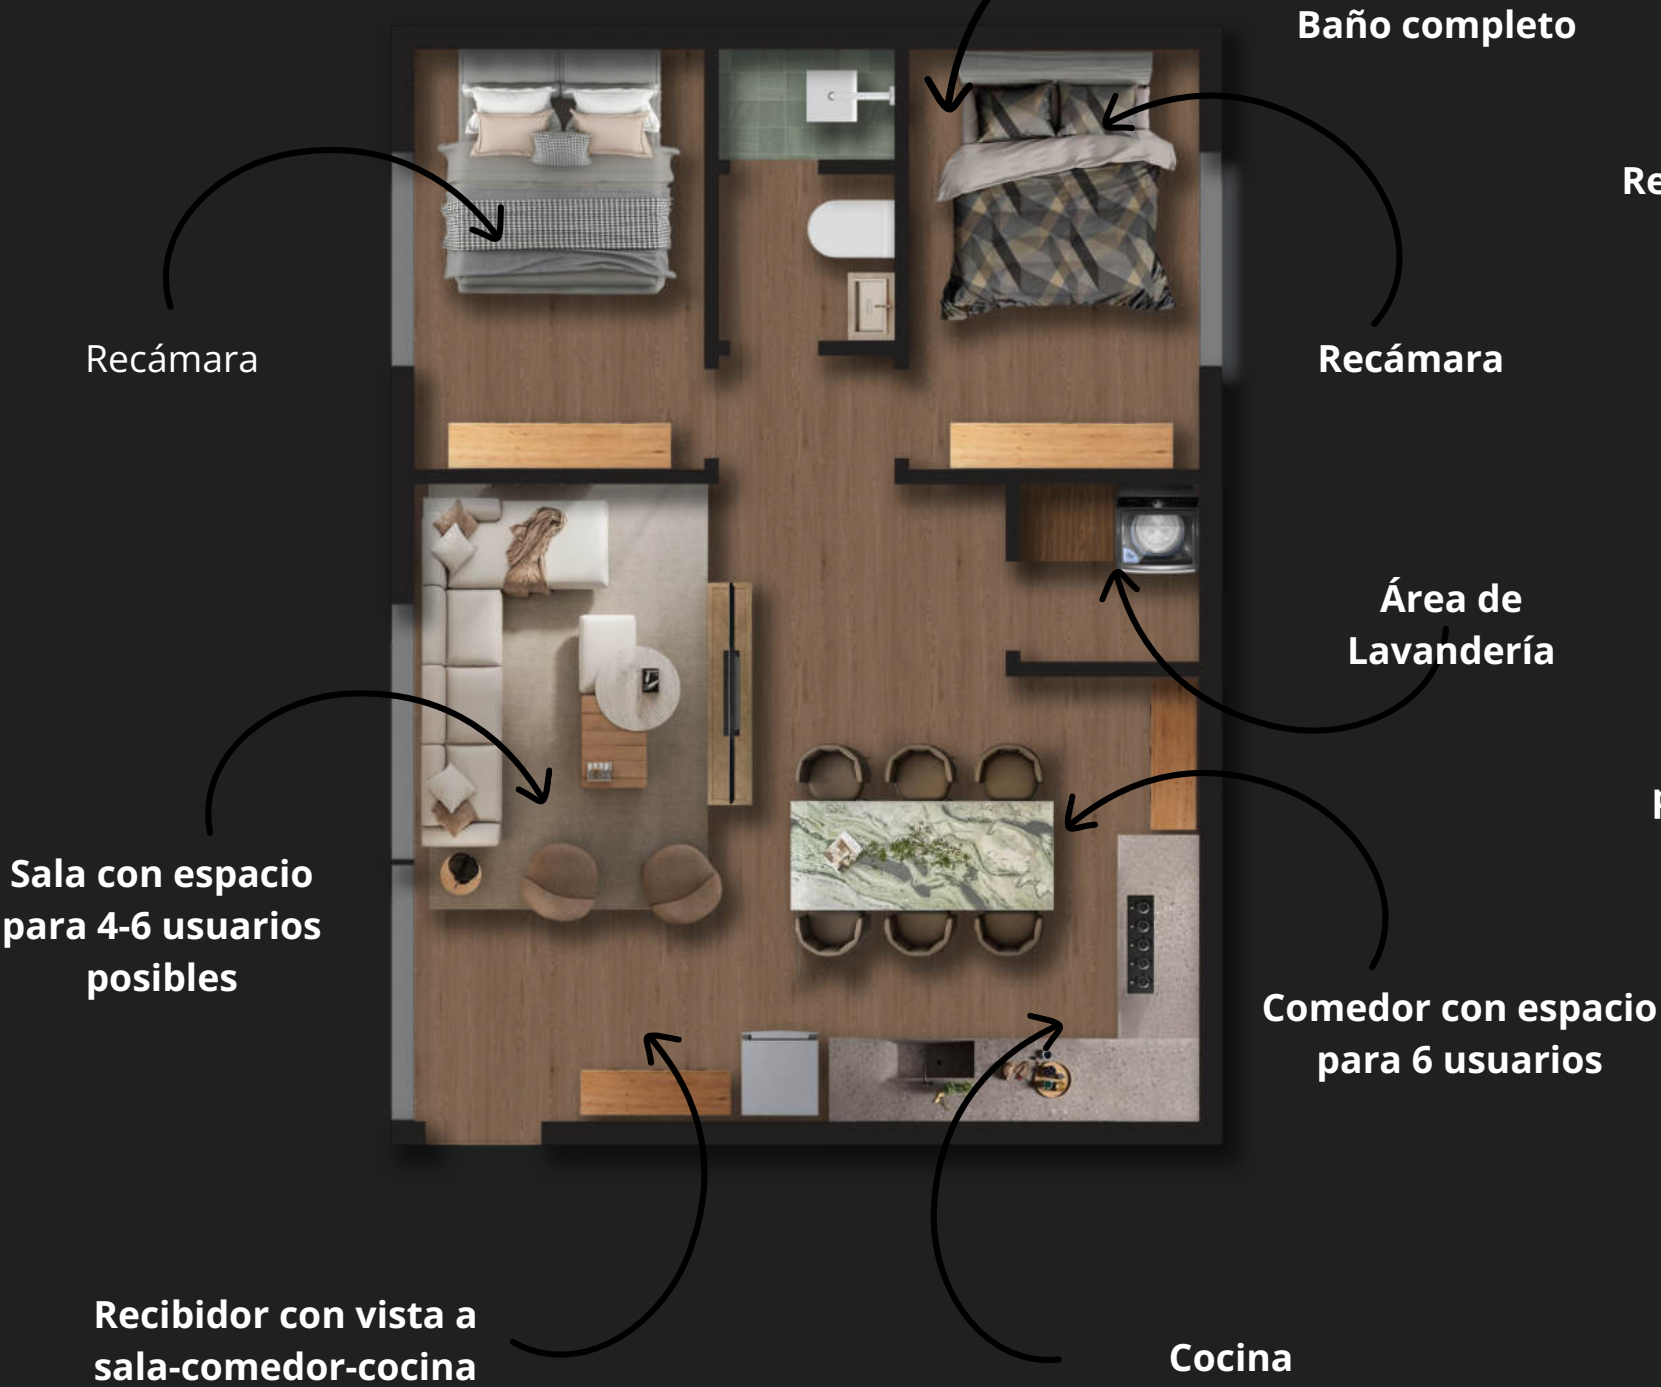

Tipo 2: 75 m²

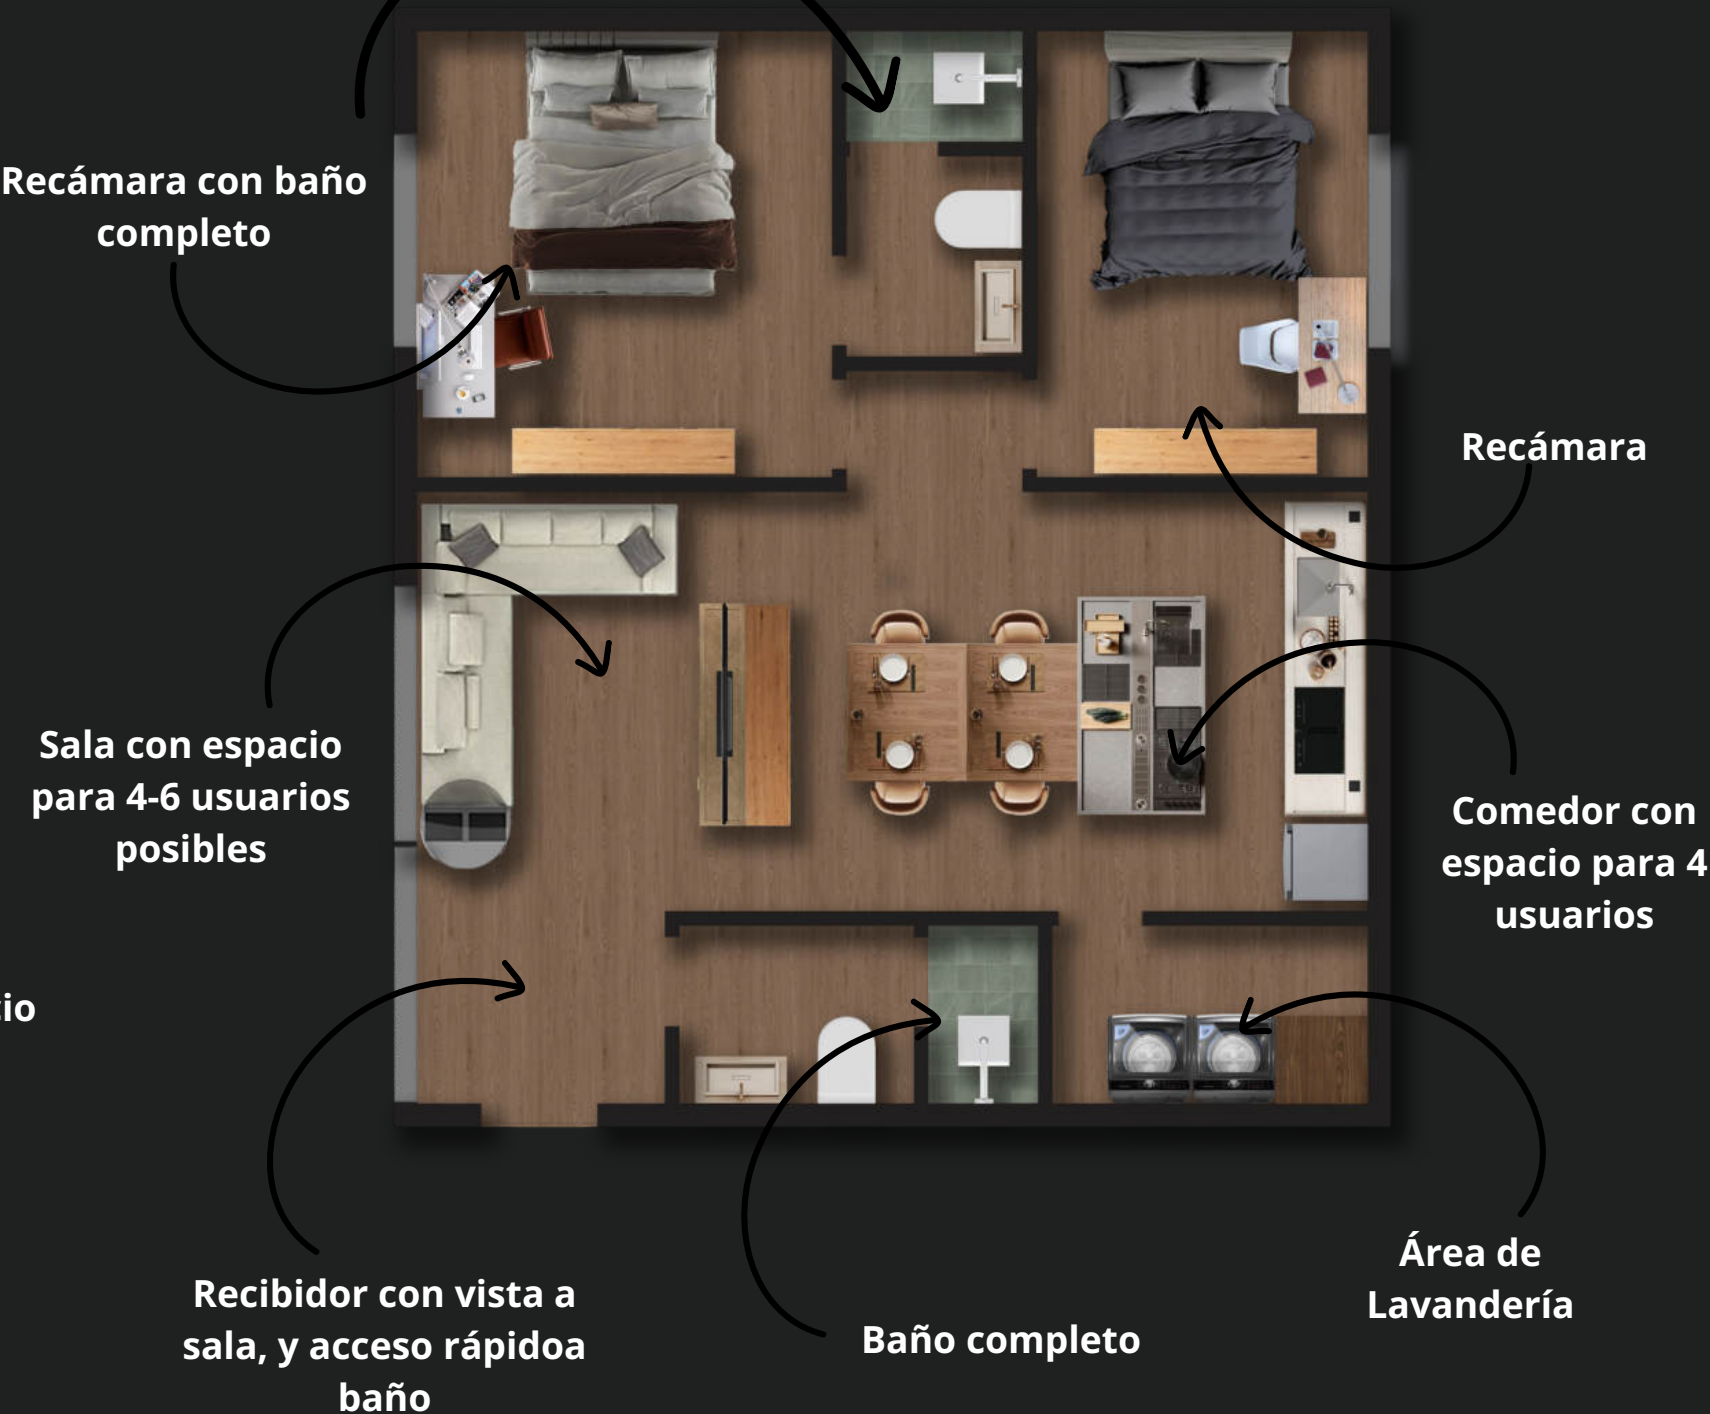


Tipo 3: 90 m²

Tipologías.



Tipología 1

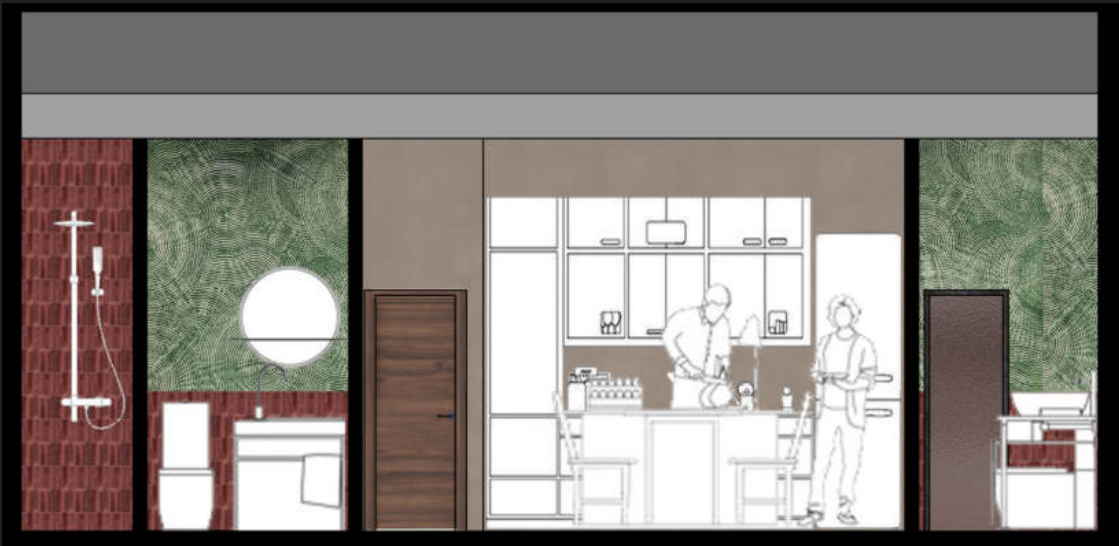

Tipología 2



Tipología 3